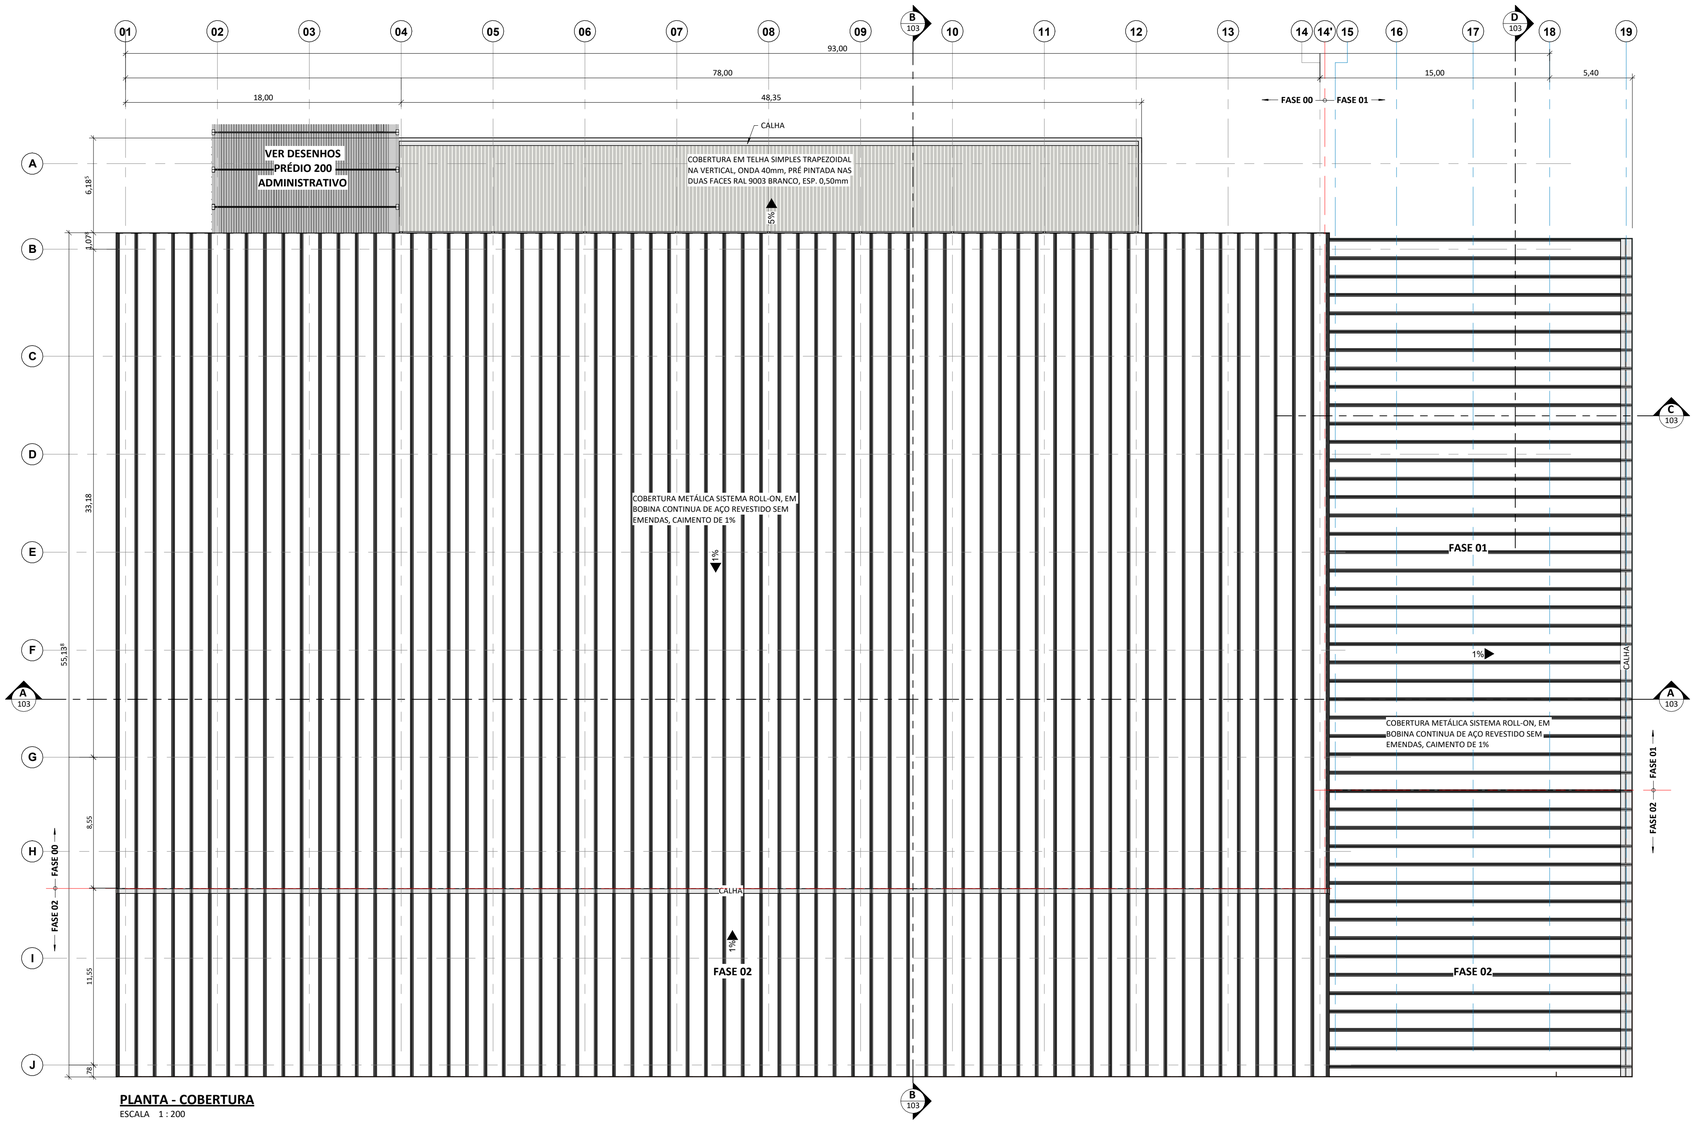


PLANTA - COBERTURA
ESCALA 1 : 200

NOTAS

1. DIMENSÕES EM METROS, EXCETO ONDE INDICADO;
2. AS COTAS DE NÍVEL REPRESENTADAS ESTÃO CONSIDERANDO O NÍVEL DO PISO ACABADO, EXCETO ONDE INDICADO;
3. TODAS AS MEDIDAS E NÍVEIS, DEVERÃO SER CONFERIDAS NO LOCAL;
4. SEMPRE CONSULTAR OS PROJETOS COMPLEMENTARES E MEMORIAIS ESPECÍFICOS, HAVENDO DIVERGÊNCIAS DE INFORMAÇÕES ENTRAR EM CONTATO COM AS EQUIPES RESPONSÁVEIS.

Nº Revisão	Descrição	Data
01	REVISÃO GERAL - INCLUSÃO FASES 01 E 02	12/02/2026

Carimbos:

Assinaturas

PROPRIETÁRIO:	AUTOR DO PROJETO:	RESPONSÁVEL TÉCNICO:
	RRT: 15046111	ART: AM20250529204
SINTRA HOLDING ADM. DE BENS IMÓVEIS PRÓPRIOS LTDA	ARQ. FRANCISCO JOSE ARTIMONTE - CAU A37074-6 SP	ENG. JOAO PEDRO JUNQUEIRA CASTRO - CREA 29133AM

Proprietário: SINTRA HOLDING ADM. DE BENS IMÓVEIS PRÓPRIOS LTDA - CNPJ 29.358.153/0001-97

Endereço: AVENIDA SOLIMÕES, Nº 250 - MAUAZINHO - MANAUS - AM

Obra:
PROJETO DE AMPLIAÇÃO

Etapa:	Projeto:
PROJETO EXECUTIVO	ARQUITETURA

Conteúdo: PRÉDIO 100 - PRODUÇÃO
PLANTA DE COBERTURA

Data: 26/03/2025

Projetista:	Coordenador:		PRANCHA Nº	Nº DE PRANCHAS
FRANCISCO ARTIMONTE	.		102	112
Desenho: CRISTIANE VIEIRA	ESCALA: Indicada	REVISÃO: 01		

INT-ARQ-PE-102-COB-R01